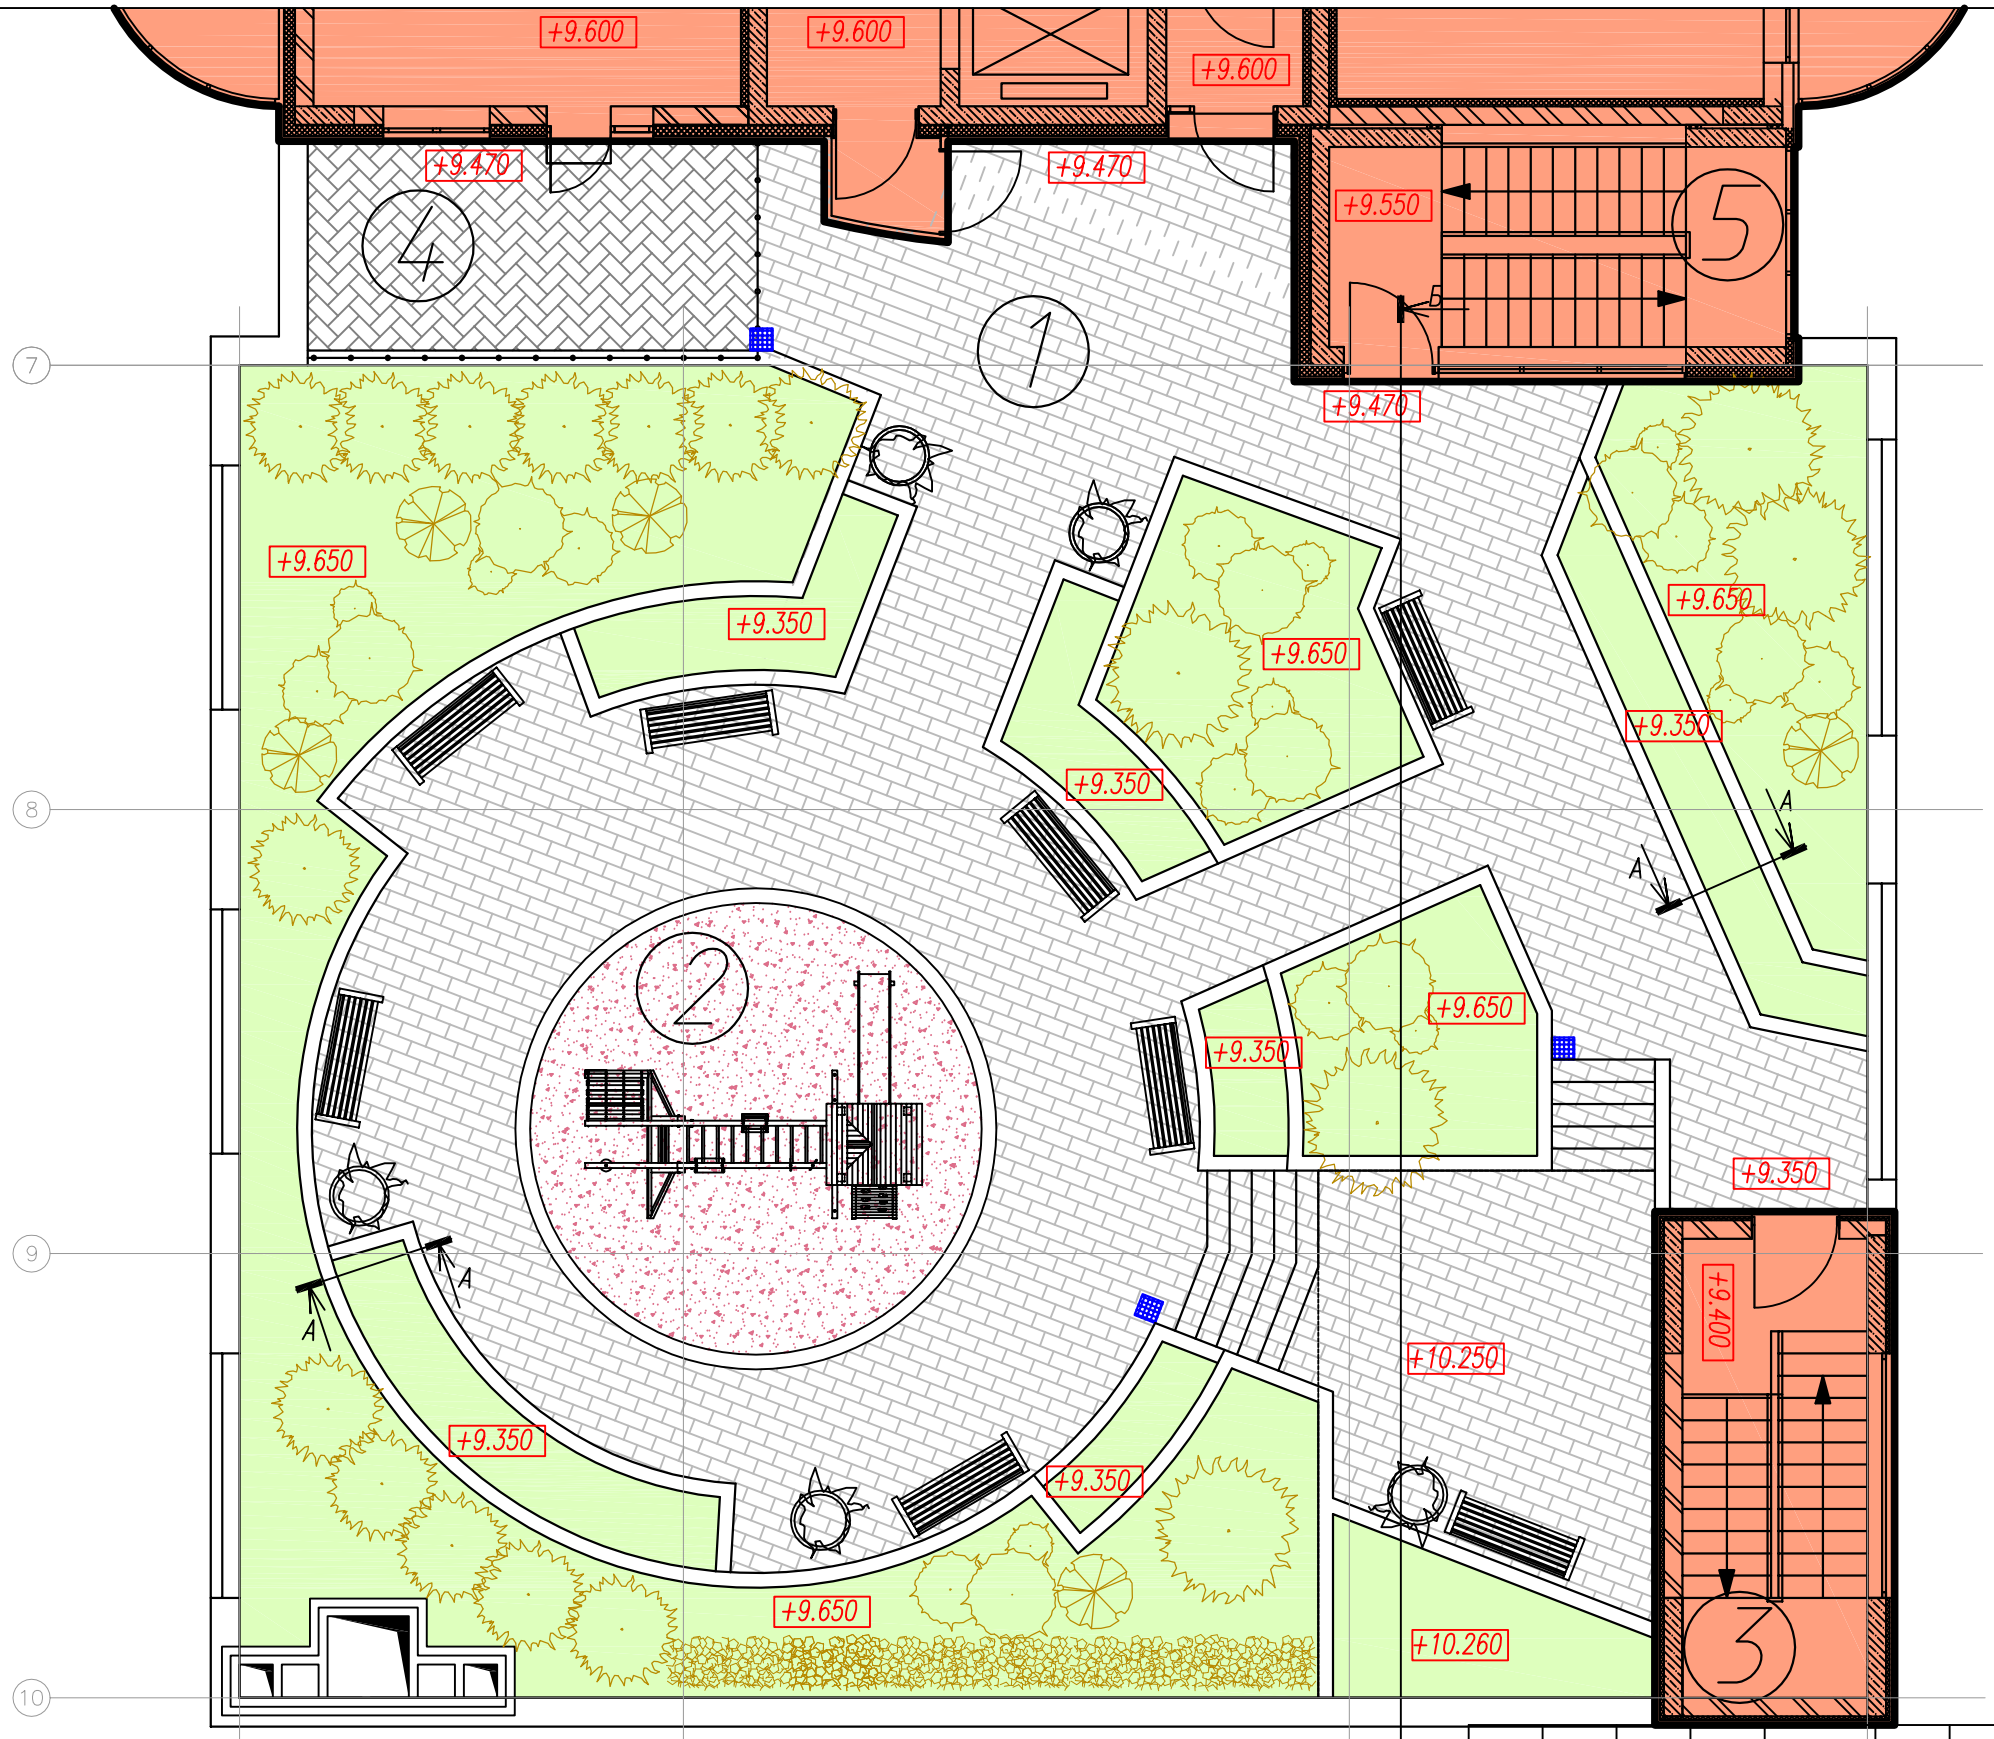

ТЕХНИКО-ЭКОНОМИЧЕСКИЕ ПОКАЗАТЕЛИ

N	Наименование	Ед.изм.	К-во
	Площадь эксплуатируемой кровли	м кв.	408,8
	в т.ч.		
1	детская площадка	м кв.	33,2
2	дорожки пешеходные	м кв.	206,7
3	терраса	м кв.	17,2
4	газон	м кв.	151,7

Принципиальное сечение А–А

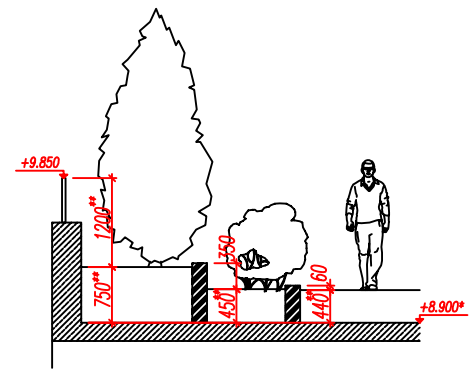

* – согласно чертежам АР
** – минимальное значение

УСЛОВНЫЕ ОБОЗНАЧЕНИЯ

- проектируемые здания
- пешеходные дорожки
- композитное покрытие
- газон
- дождеприемник

ЭКСПЛИКАЦИЯ ЗДАНИЙ И СООРУЖЕНИЙ

N по ГП	Наименование	Кол-во	Примечания
1	Эксплуатируемая кровля	1	Проектируемый
2	Детская площадка	1	Проектируемый
3	Выход из автостоянки	1	Проектируемая
4	Терраса	1	Проектируемая
5	Многоквартиный жилой дом	1	Проектируемая

Схематическое сечение Б–Б

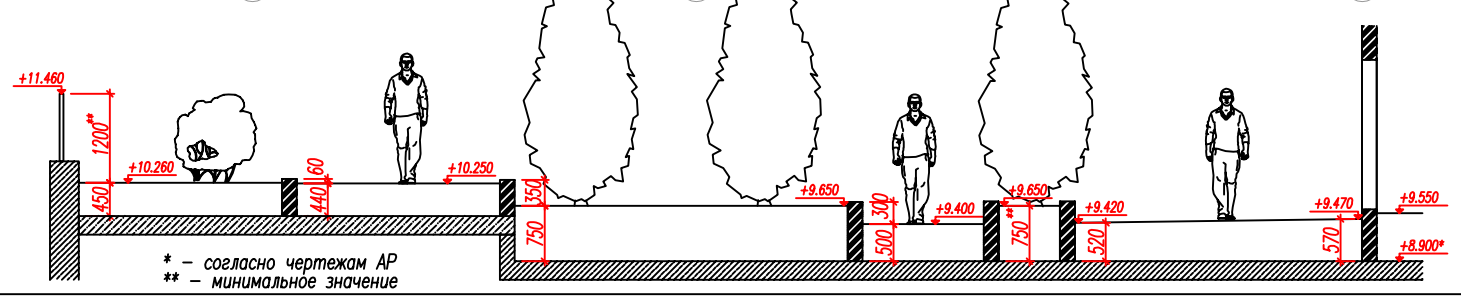

* – согласно чертежам АР
** – минимальное значение

Изм.	Кол.уч.	Лист	§док.	Подп.	Дата
ГАП		Нечаев			
АРХИТЕКТОР		Львова			
Дизайнер		Лукина			
Инженер		Абидина			

Заказчик: частное лицо

Элитный жилой дом со встроенно-пристроенными помещениями по адресу: г.Пермь, ул.Луначарского, 32А

Эксплуатируемая кровля. 4 этаж

Стадия	Лист	Листов
Р		

Генеральный план
М 1:100

Формат А3