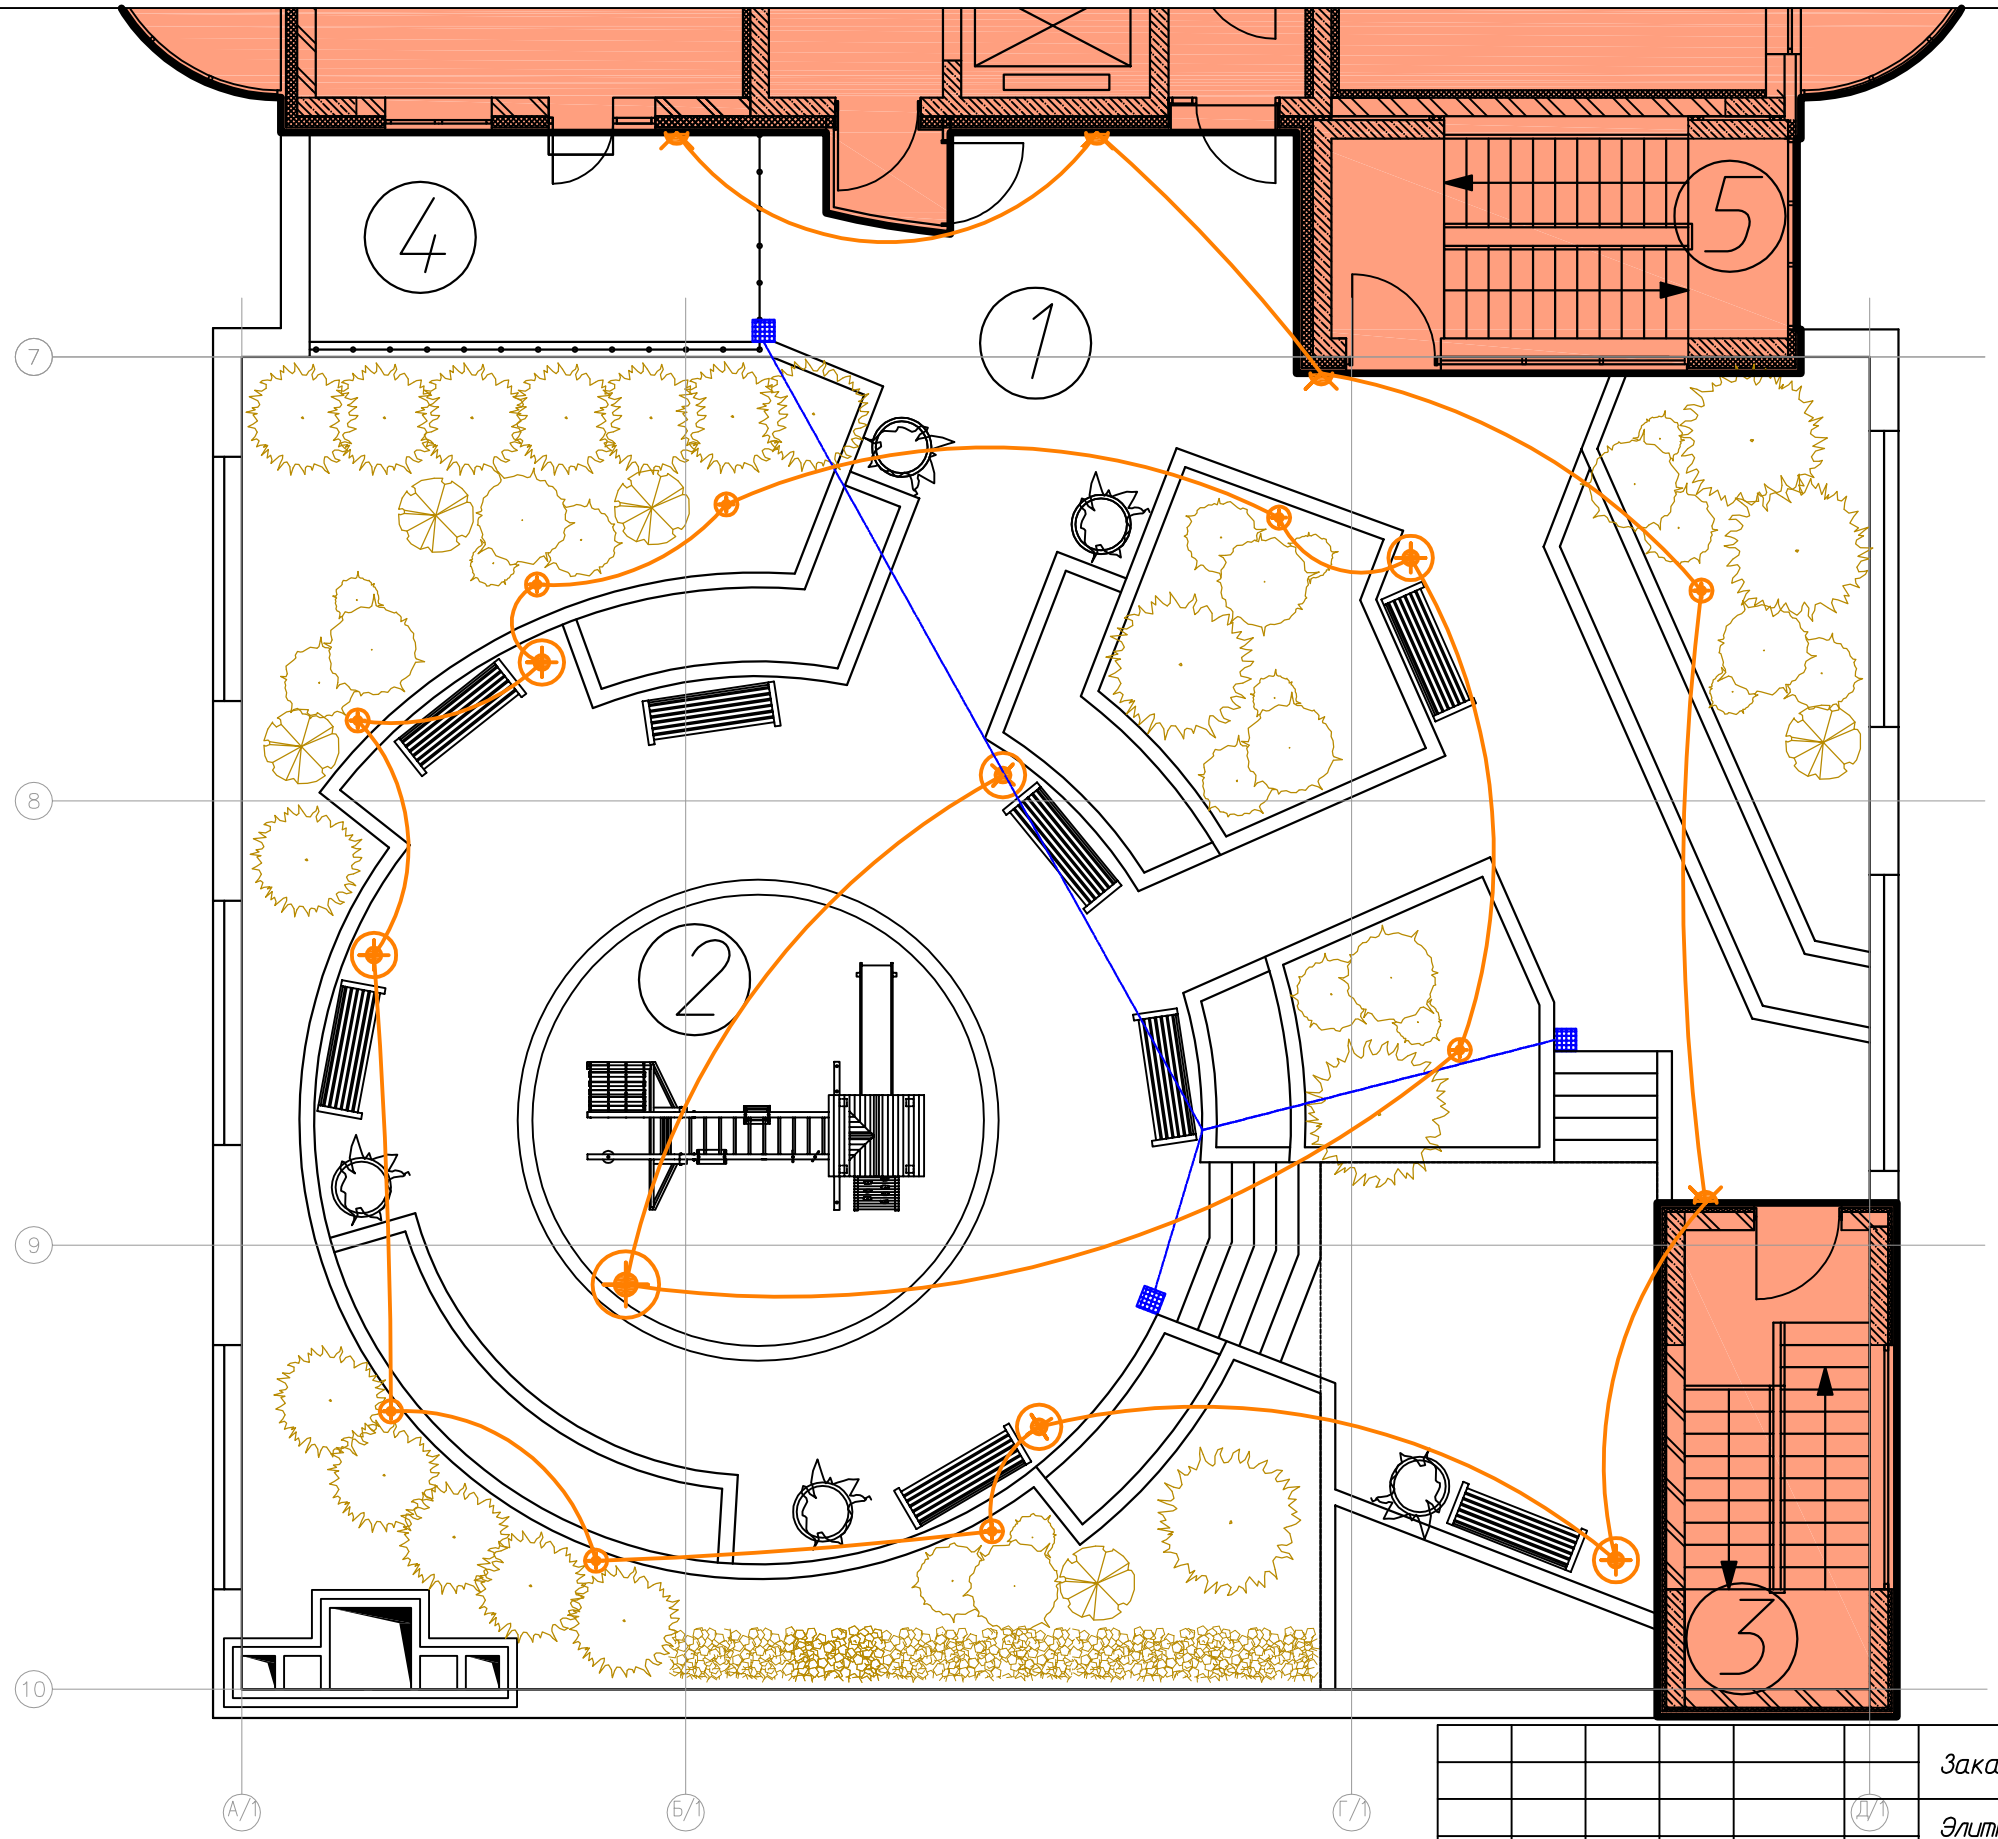

ТЕХНИКО-ЭКОНОМИЧЕСКИЕ ПОКАЗАТЕЛИ

N	Наименование	Ед.изм.	К-во
	Площадь эксплуатируемой кровли	м кв.	408,8
	в т.ч.		
1	детская площадка	м кв.	33,2
2	дорожки пешеходные	м кв.	206,7
3	терраса	м кв.	17,2
4	газон	м кв.	151,7

ВЕДОМОСТЬ ОБОРУДОВАНИЯ

Поз.	Наименование породы или вида насаждения	Произв.	Кол.	Примечание
1	2	3	4	5
1	Детский спортивный комплекс	-	1	-
2	Скамья	-	8	-
3	Вазон	-	5	-
4	Дождеприемник точечный	-	3	-
5	Светильник декоративный	-	9	-
6	Фонарь	-	6	-
7	Светильник настенный	-	4	-
8				

ЭКСПЛИКАЦИЯ ЗДАНИЙ И СООРУЖЕНИЙ

N по ГП	Наименование	Кол-во	Примечания
1	Эксплуатируемая кровля	1	Проектируемый
2	Детская площадка	1	Проектируемый
3	Выход из автостоянки	1	Проектируемая
4	Терраса	1	Проектируемая
5	Многоквартиный жилой дом	1	Проектируемая

УСЛОВНЫЕ ОБОЗНАЧЕНИЯ

- проектируемые здания
- пешеходные дорожки
- композитное покрытие
- газон
- дождеприемник
- ливневая канализация
- светильник декоративный
- фонарь
- светильник настенный
- электрическая сеть

Изм.	Кол.уч.	Лист	№док.	Подп.	Дата
ГАП		Нечаев			
АРХИТЕКТОР		Львова			
Дизайнер		Лукина			
Инженер		Абидина			

Заказчик: частное лицо

Элитный жилой дом со встроенно-пристроенными помещениями по адресу: г.Пермь, ул.Луначарского, 32А

Эксплуатируемая кровля. 4 этаж

Стадия	Лист	Листов
Р		

План освещения и оборудования территории

М 1:100

Формат А3